


Разрез 1-1 М 1:100

Битумная черепица (Катепал)
 Подкладочный слой – рудероид
 Сплошной настил
 Конробрешетка
 Гидроизоляционная мембрана
 Теплоизоляция
 Пароизоляция
 Обрешетка
 Внутренняя облицовка

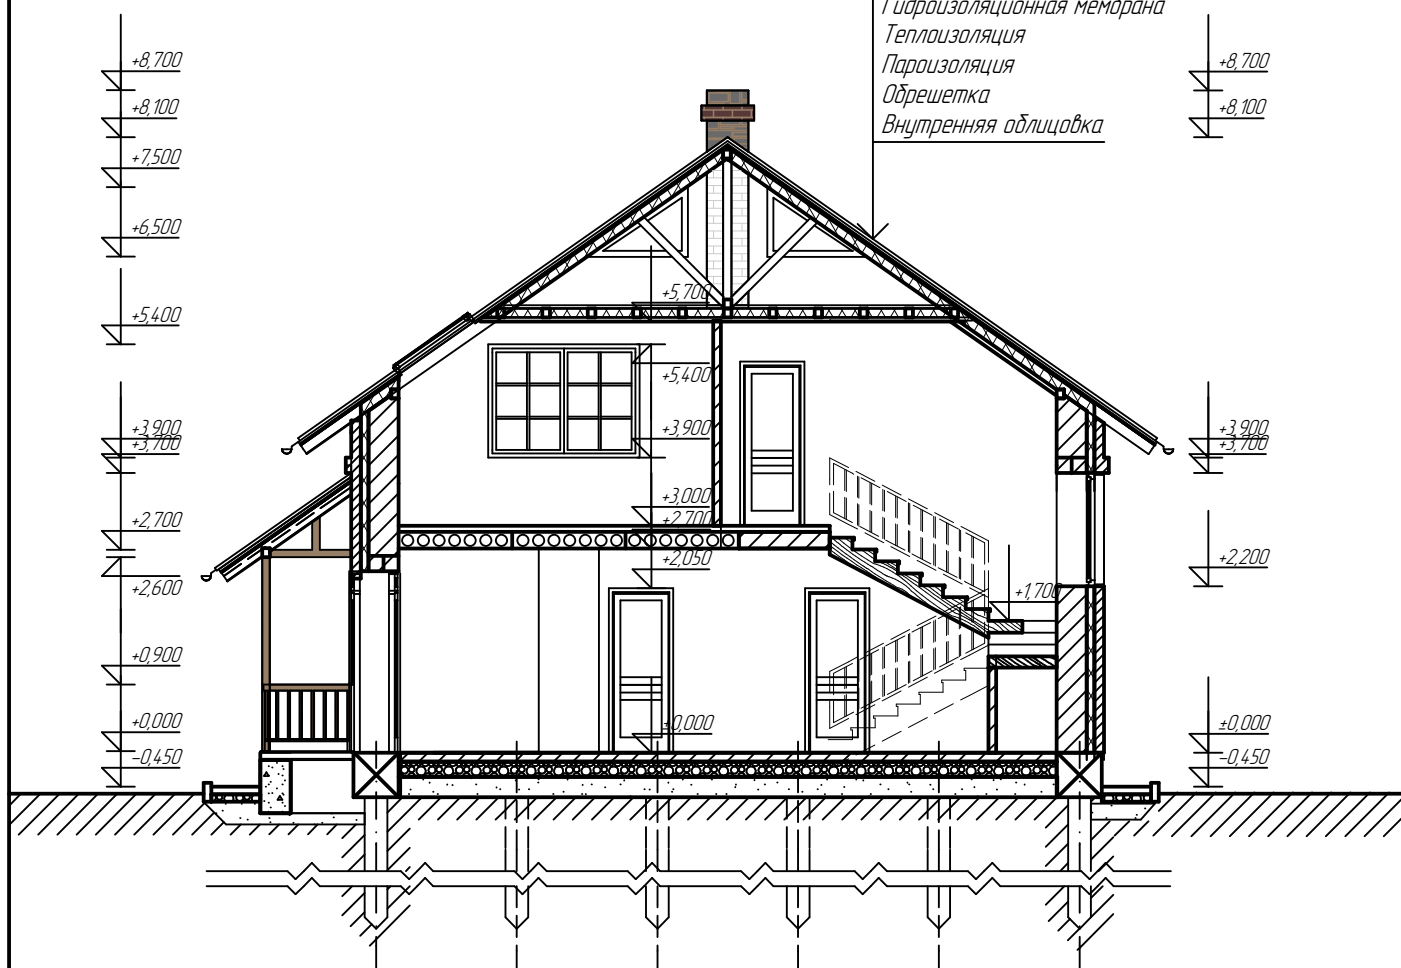

			2016	Постановление № _____			АР		
	№ документа	Подпись	Дата	Заказчик: Разумов А.В.					
Архитектор	Чеснокова Н.И.								
				ПАСПОРТ индивидуального жилого дома, расположенного по адресу: Тамбовская обл., Тамбовский р-н, д.Красненькая, ул. 2-ая почтовая			Стадия	Лист	Листов
							ЭП	5	13
				Разрез 1-1 М 1:100			 www.dom-design-decor.ru		